
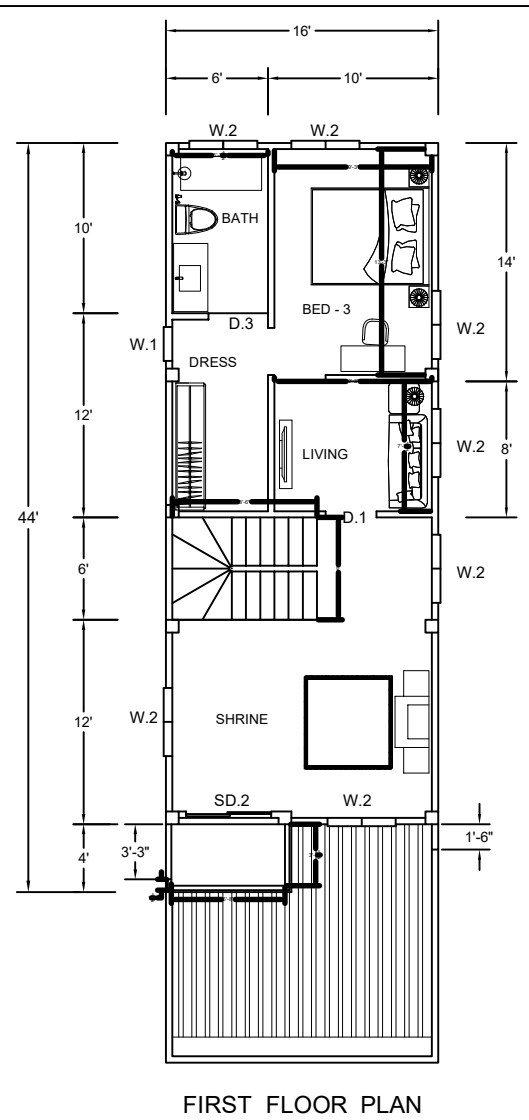


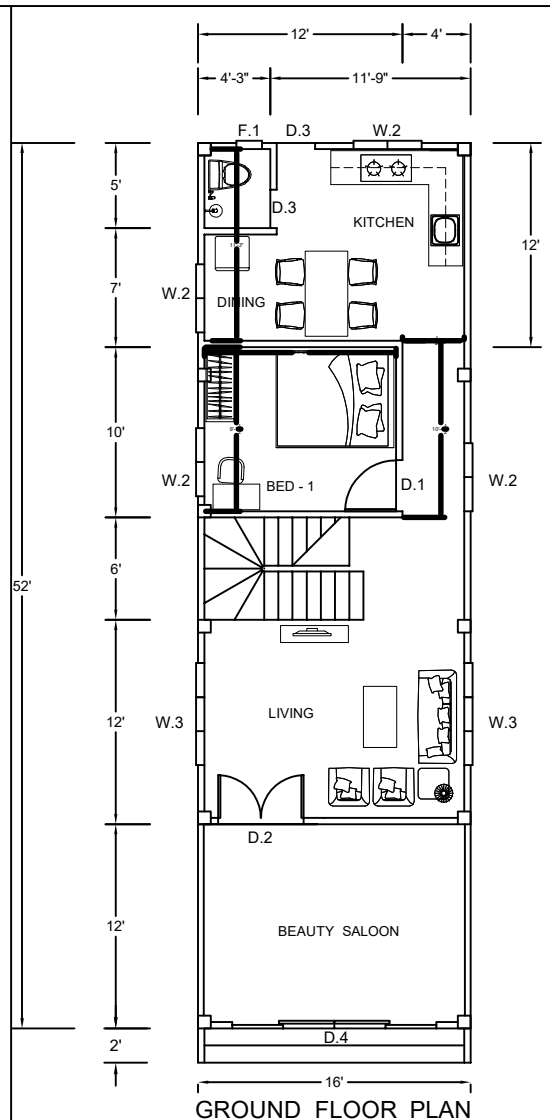

REVISION NO.	OWNER/ APPLICANT	PROJECT PROPOSED (3) STOREYED R.C RESIDENTIAL BUILDING		TITLE GROUND FLOOR & FIRST FLOOR PLAN		DRAWING NO. A-101
		Design by	Approve by	Scale 1" = 8' 0"	Date.	