


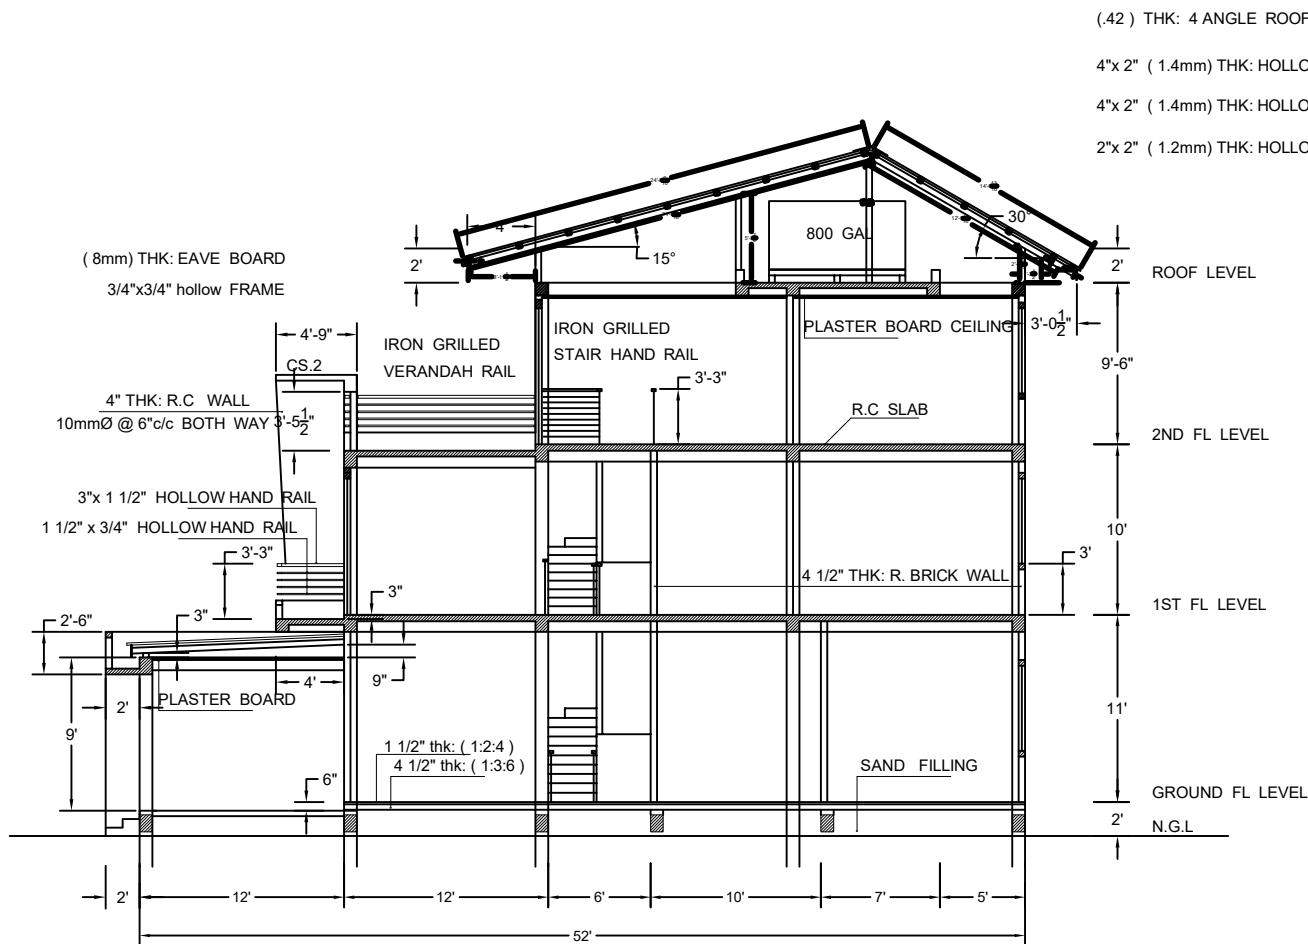


LONGITUDINAL SECTION

(.42) THK: 4 ANGLE ROOFING SHEET

4"x 2" (1.4mm) THK: HOLLOW COLUMN

4"x 2" (1.4mm) THK: HOLLOW RAFTER

2"x 2" (1.2mm) THK: HOLLOW PURLIN

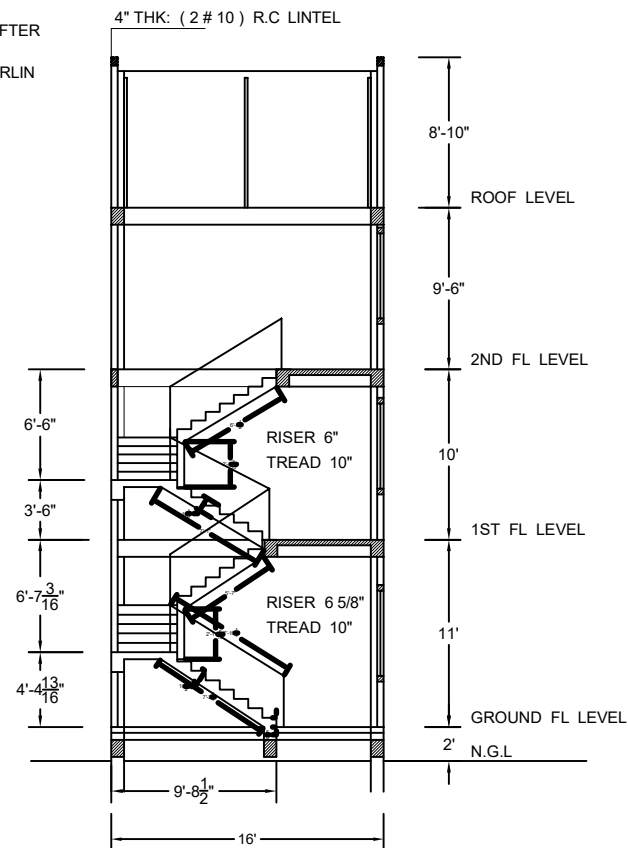

CROSS SECTION

REVISION NO.	OWNER/ APPLICANT	PROJECT	TITLE	DRAWING NO.
		PROPOSED (3) STOREYED R.C RESIDENTIAL BUILDING	SECTION DETAIL	A-301
		Design by	Approve by	Scale 1" = 8' 0"
				Date.