

KAN NAR LANN,MAGWAY

33' 6"X36' 6" 2.5 STOREYED BUILDING

ARCHITECTURAL DRAWING

7th , February ,2026



OWNER / APPLICANT

PROJECT

PROPOSED
(4) STOREYED
R.C.C BUILDING

BLOCK NO.

LOT NO.

MAGWAY TOWNSHIP

SUBJECT

SCALE

AS SHOWN.

SHEET NO.

DATE


7.02.2026



L.S

L.C

S.E.C

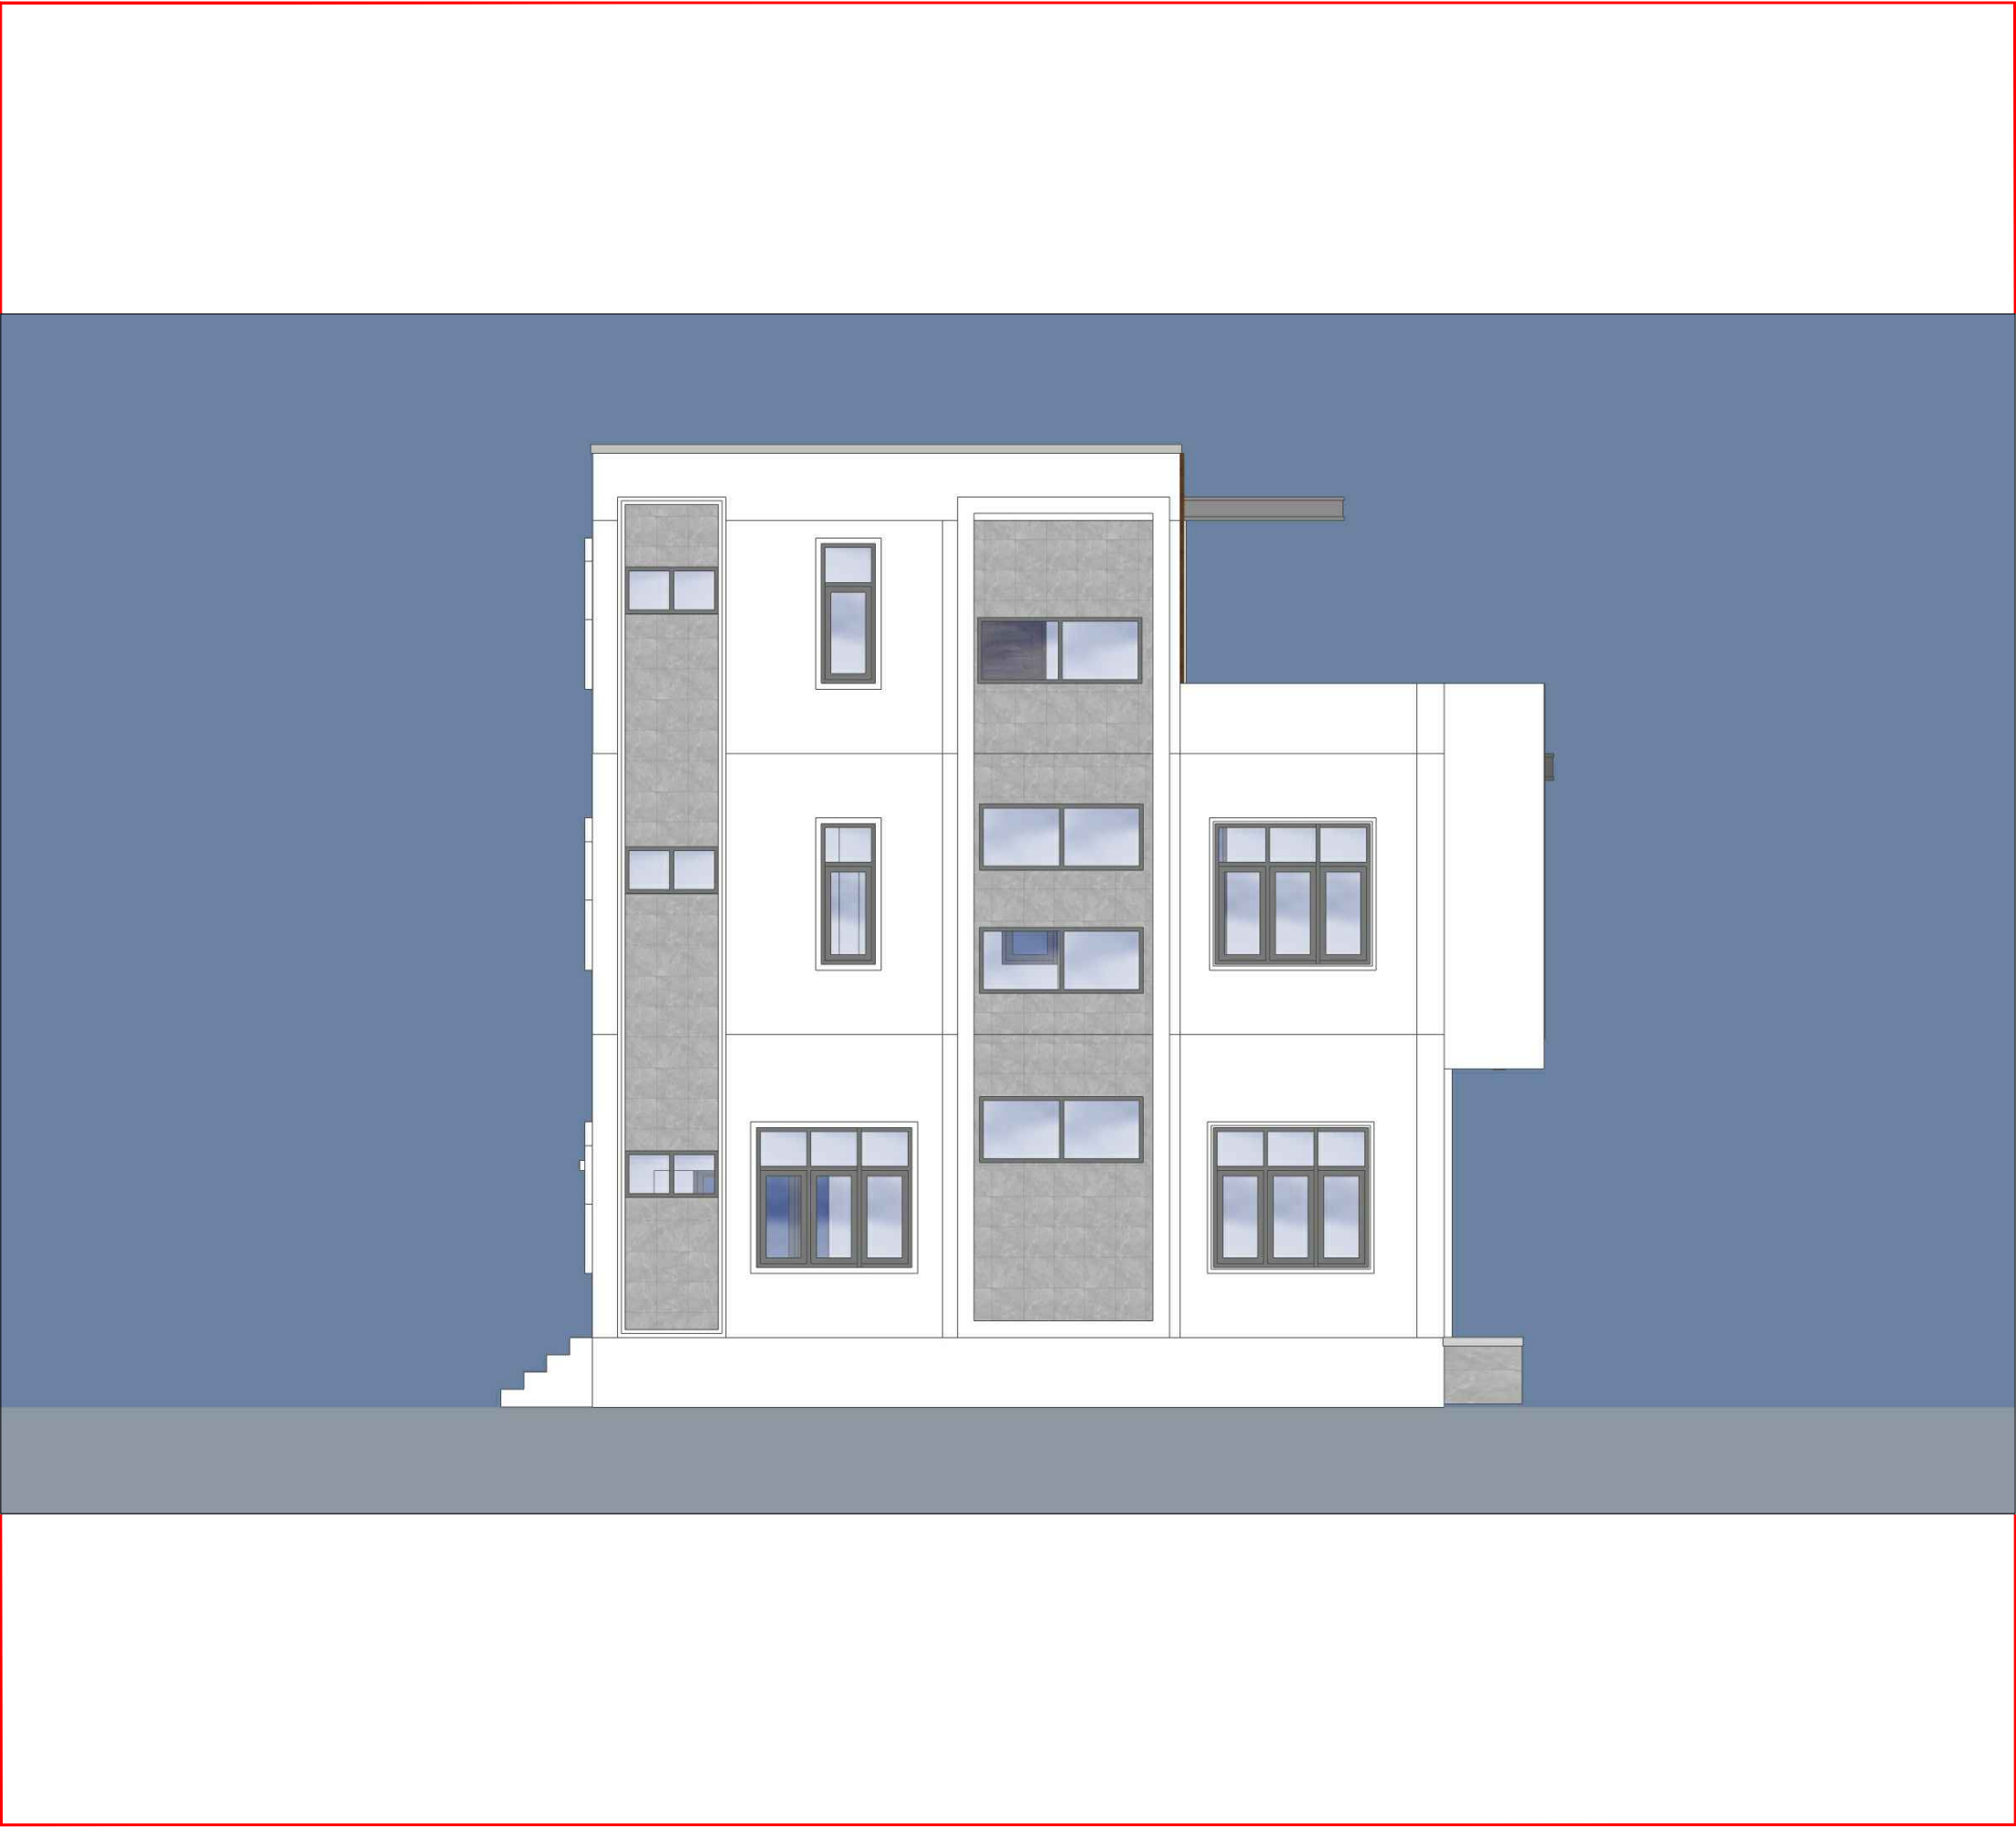

OWNER / APPLICANT

PROJECT	PROPOSED (4) STOREYED R.C.C BUILDING	
	BLOCK NO.	
	LOT NO.	
	MAGWAY TOWNSHIP	


SUBJECT		
---------	--	--

SCALE	AS SHOWN.	SHEET NO. ○
DATE	7.02.2026	


L.S

L.C


S.E.C

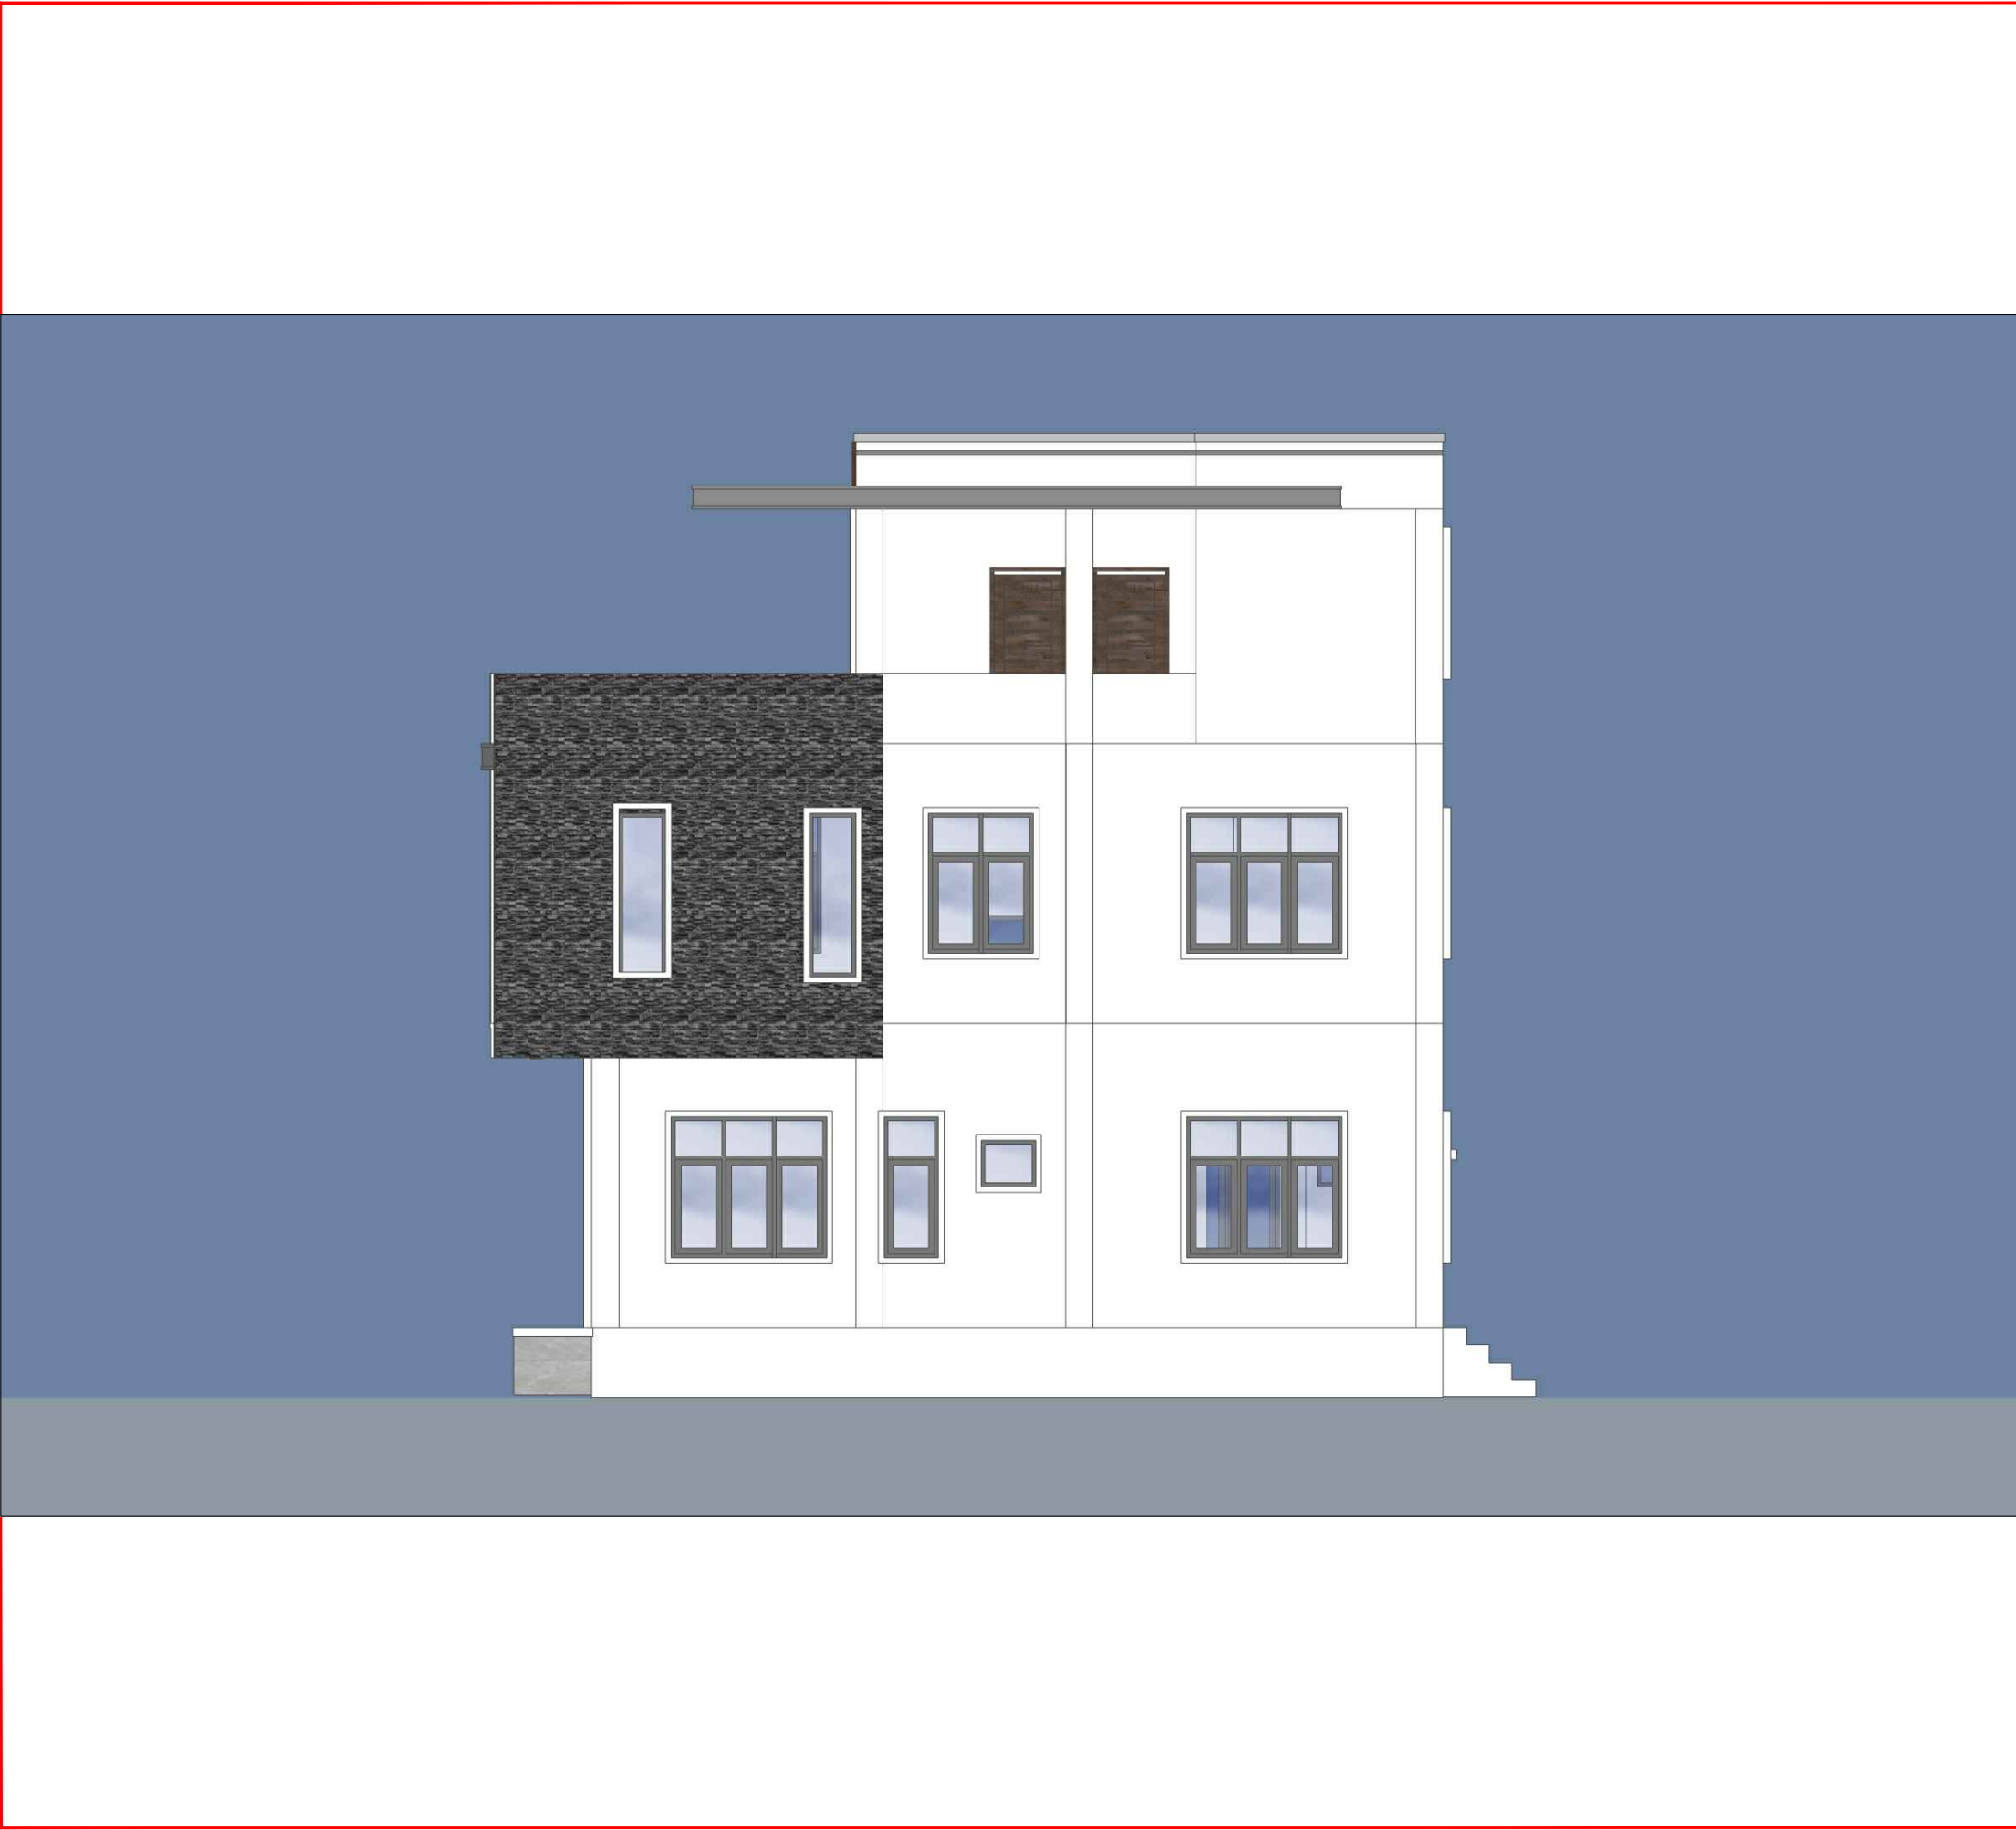

OWNER / APPLICANT		
PROJECT	PROPOSED (4) STOREYED R.C.C BUILDING	
	BLOCK NO.	
	LOT NO.	
	MAGWAY TOWNSHIP	
SUBJECT		
SCALE	AS SHOWN.	SHEET NO. ○
DATE	7.02.2026	
L.S		
L.C		
S.E.C		

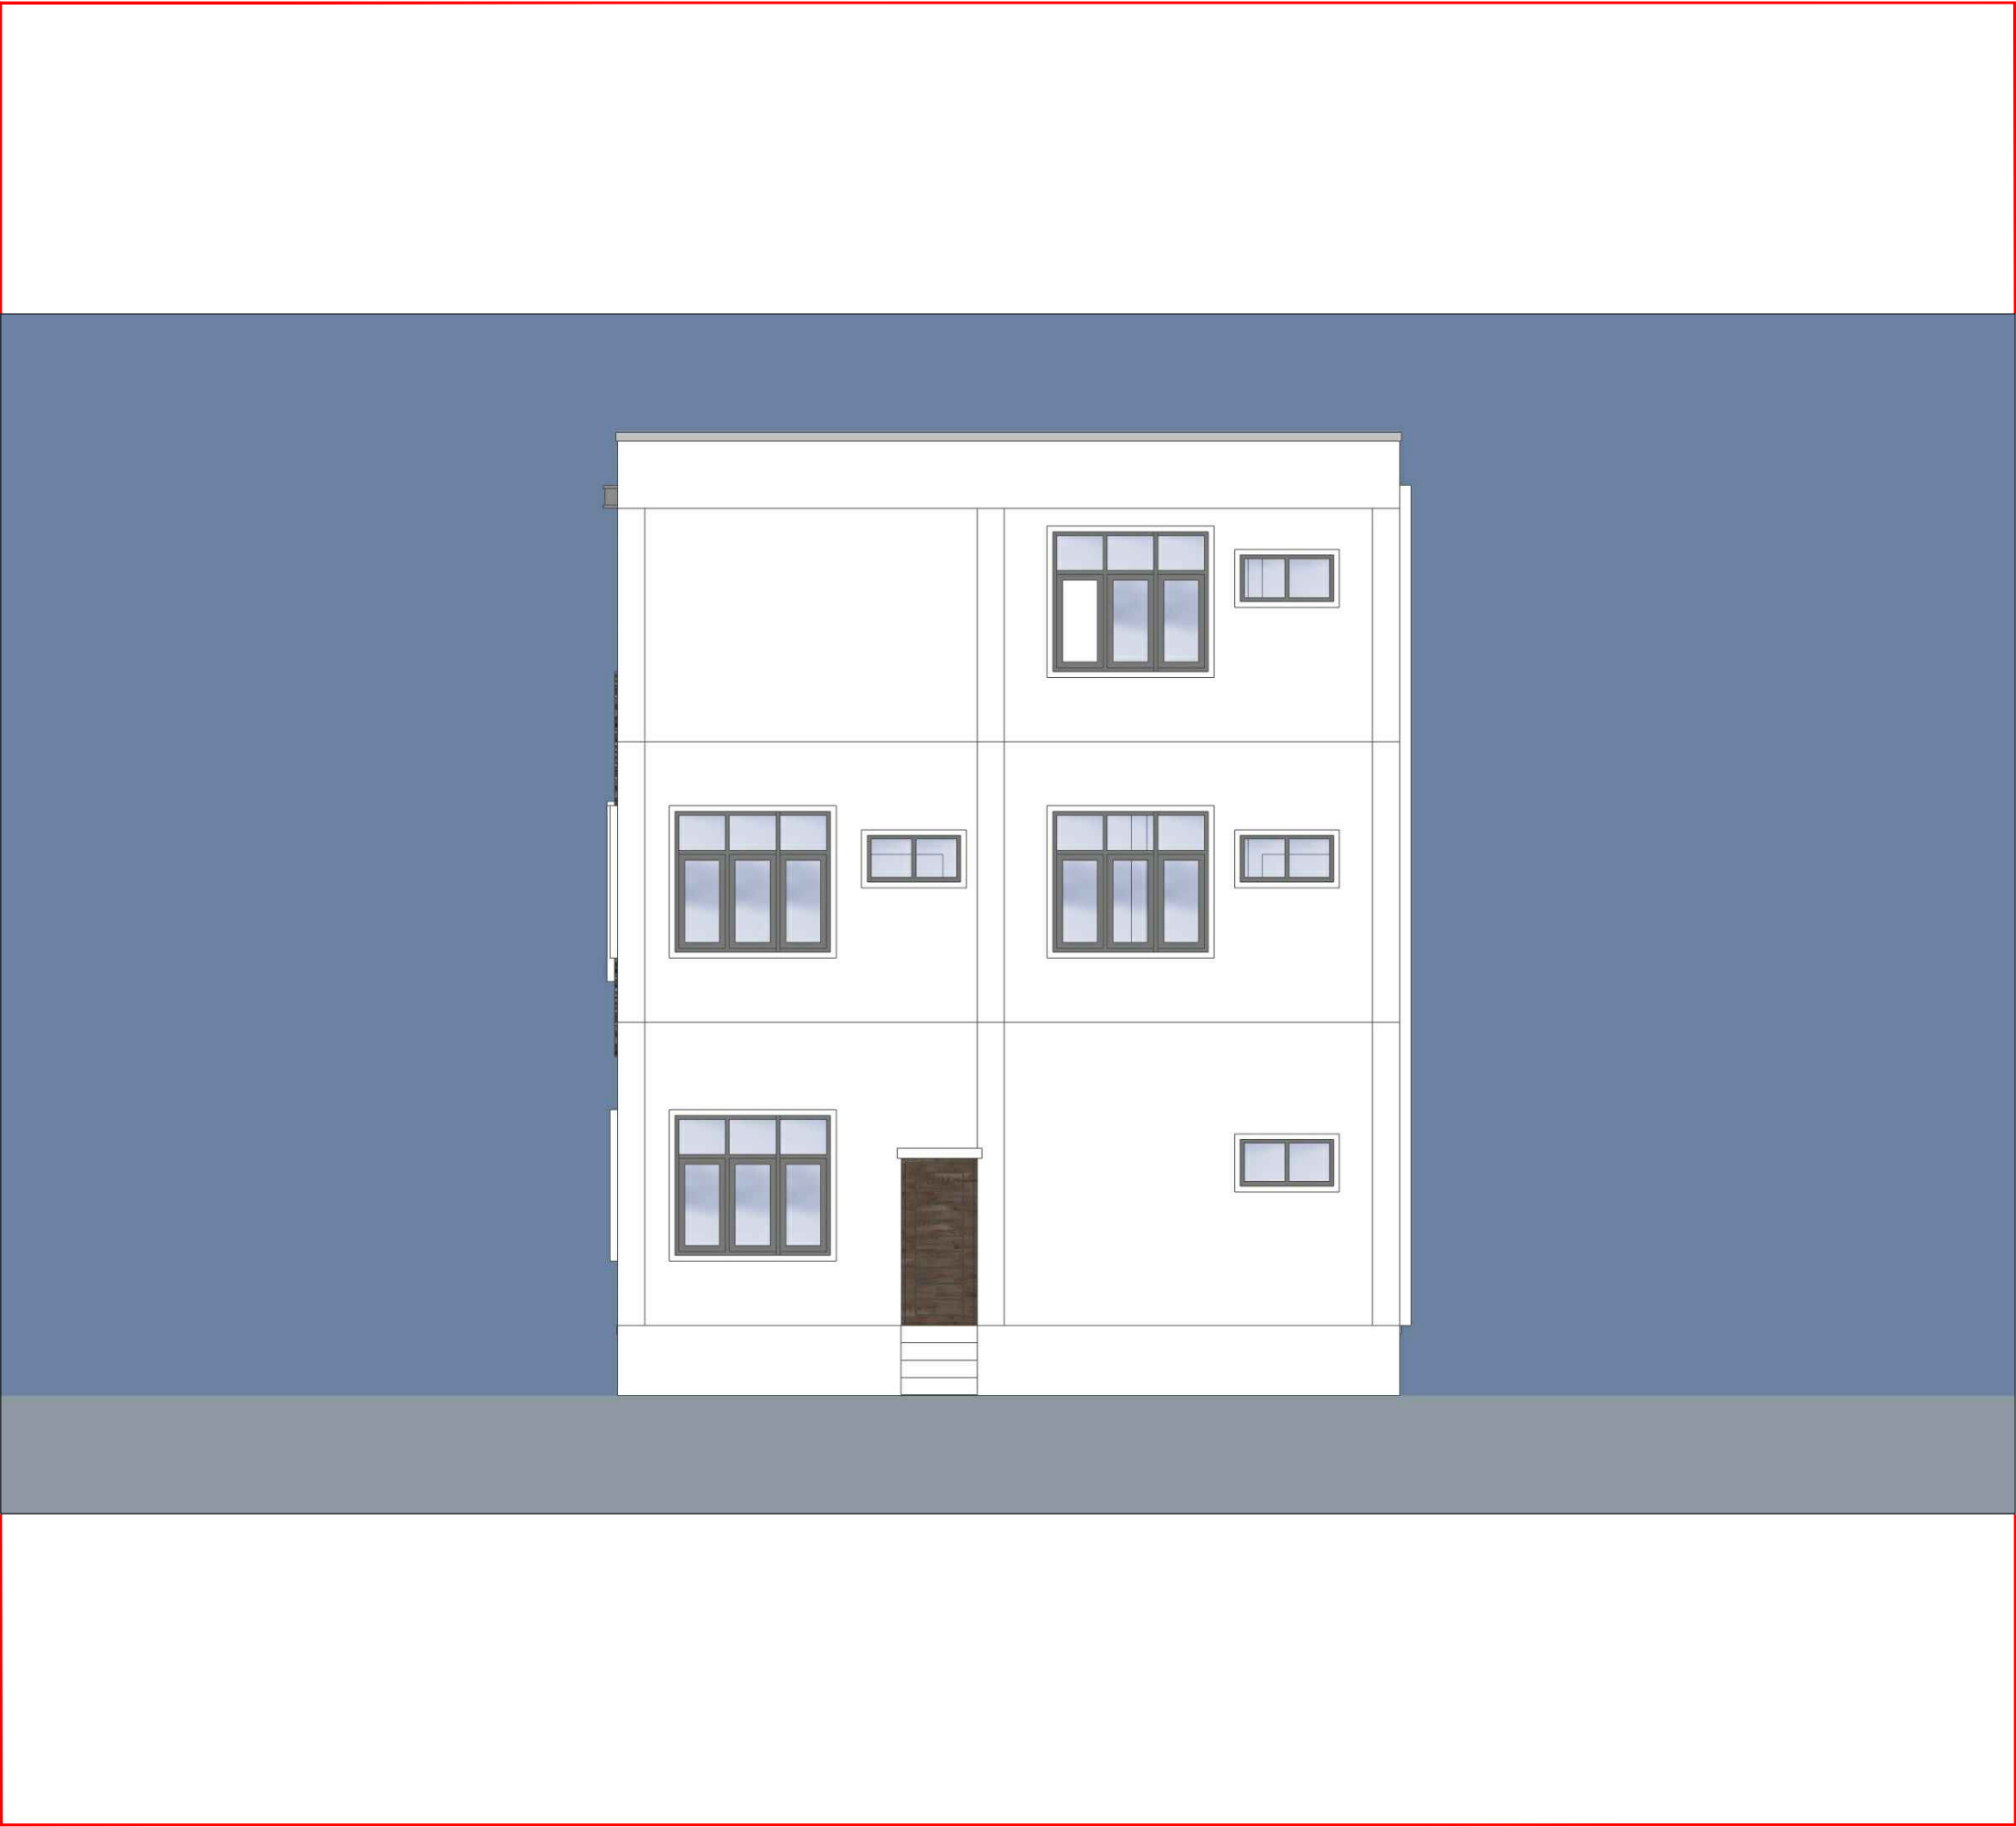

OWNER / APPLICANT		
PROJECT	PROPOSED (4) STOREYED R.C.C BUILDING	
	BLOCK NO.	
	LOT NO.	
	MAGWAY TOWNSHIP	
SUBJECT		
SCALE	AS SHOWN.	SHEET NO. ○
DATE	7.02.2026	
L.S		
L.C		
S.E.C		

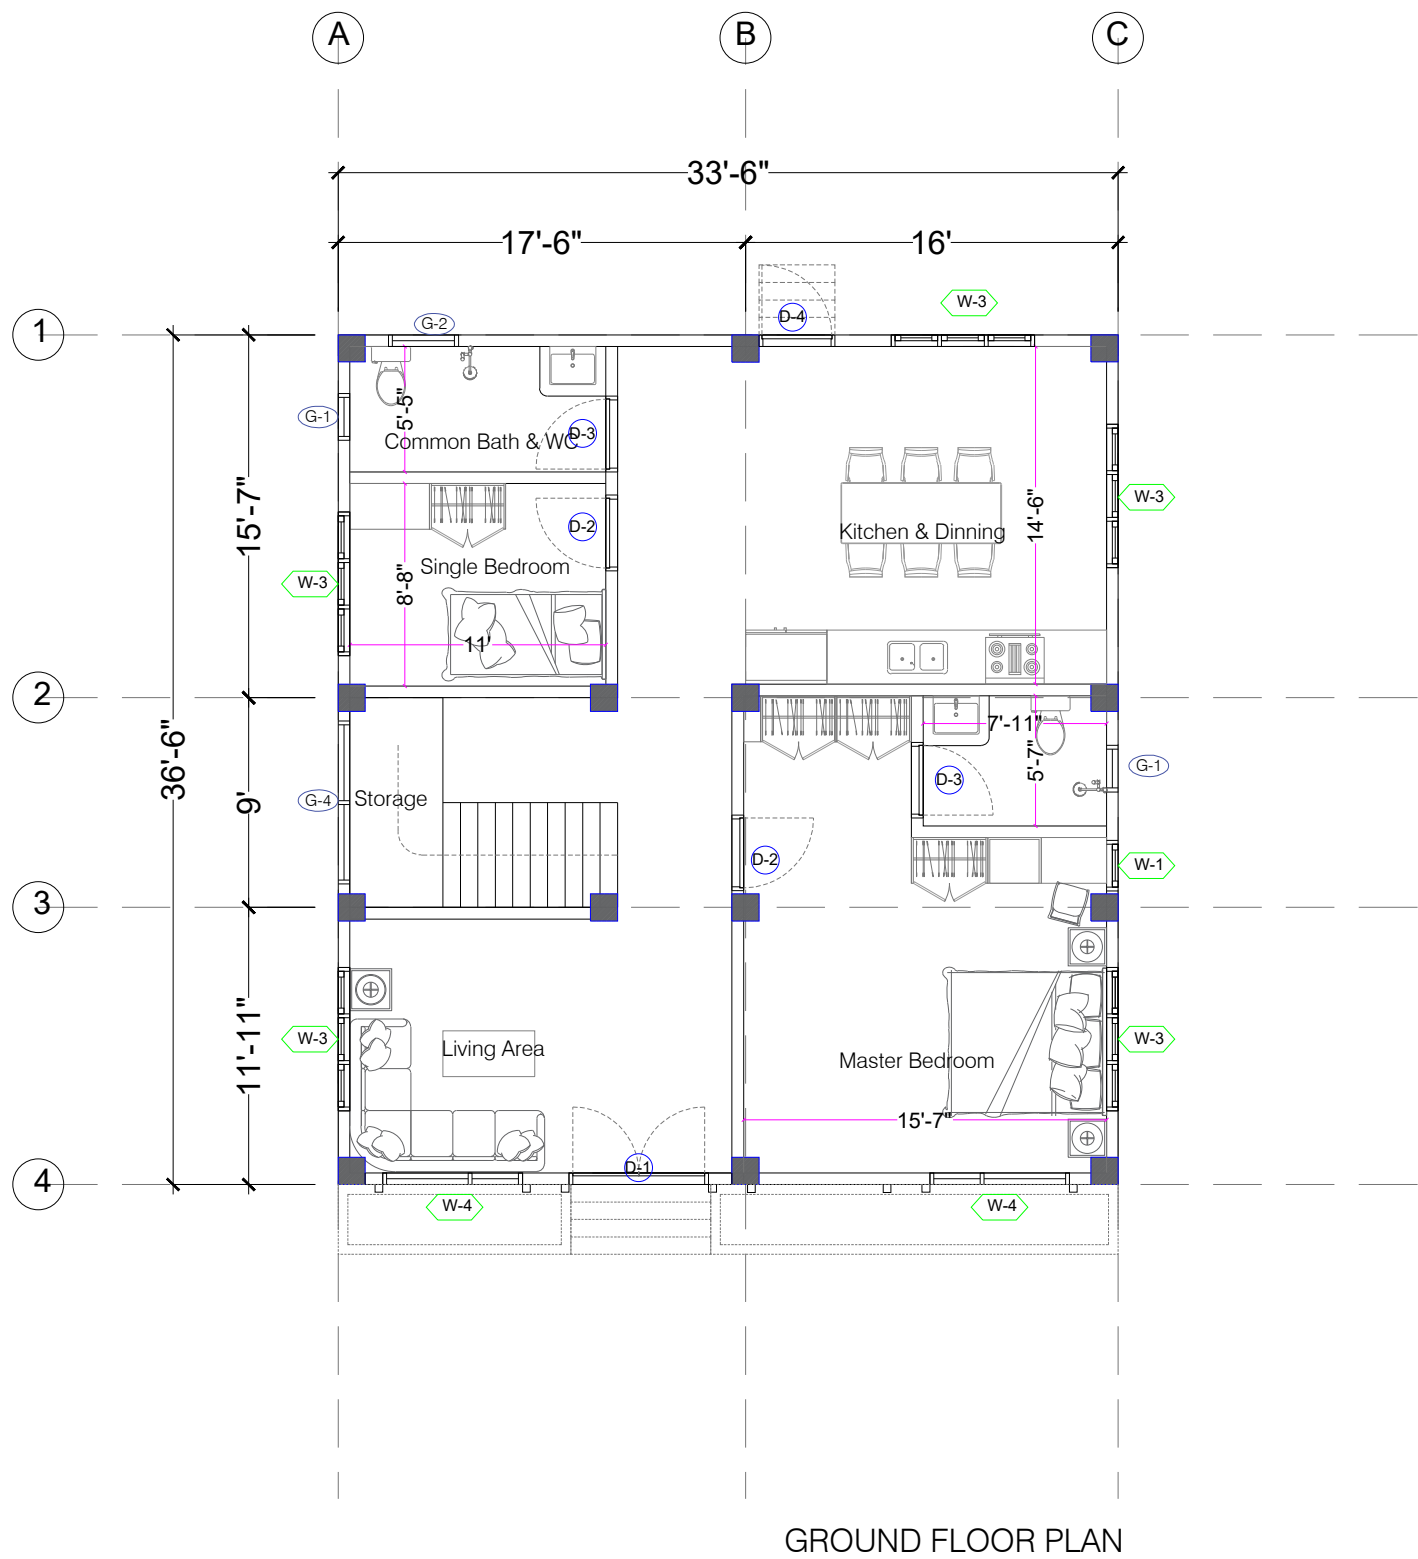

OWNER / APPLICANT

PROJECT
PROPOSED
(4) STOREYED
R.C.C BUILDING

BLOCK NO.

LOT NO.

MAGWAY TOWNSHIP

SUBJECT
GROUND FLOOR PLAN

SCALE
AS SHOWN.

SHEET NO.


DATE
7.02.2026

01

L.S

L.C

S.E.C

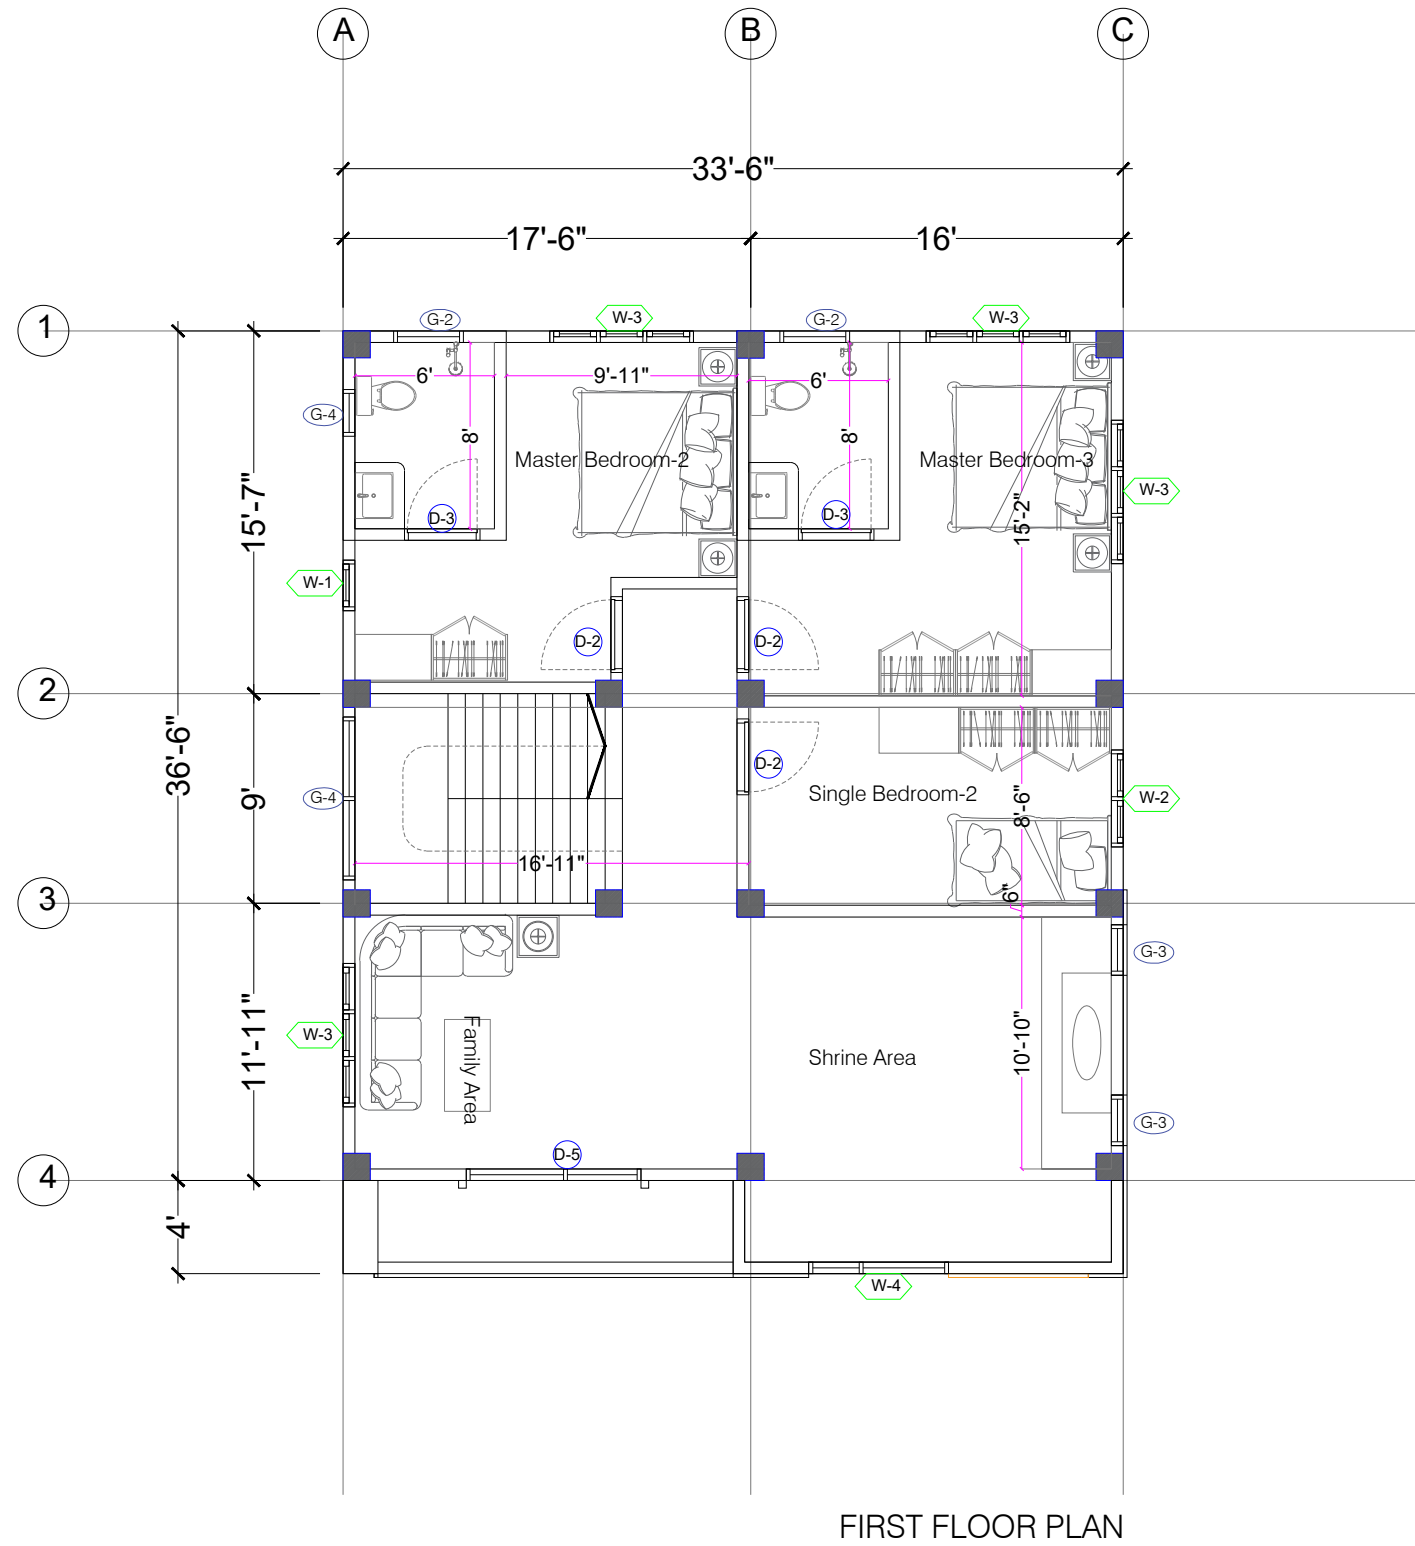

OWNER / APPLICANT

PROJECT
PROPOSED
(4) STOREYED
R.C.C BUILDING

BLOCK NO.

LOT NO.

MAGWAY TOWNSHIP

SUBJECT
FIRST FLOOR PLAN

SCALE
AS SHOWN.

DATE
7.02.2026


SHEET NO.

02

L.S

L.C

S.E.C

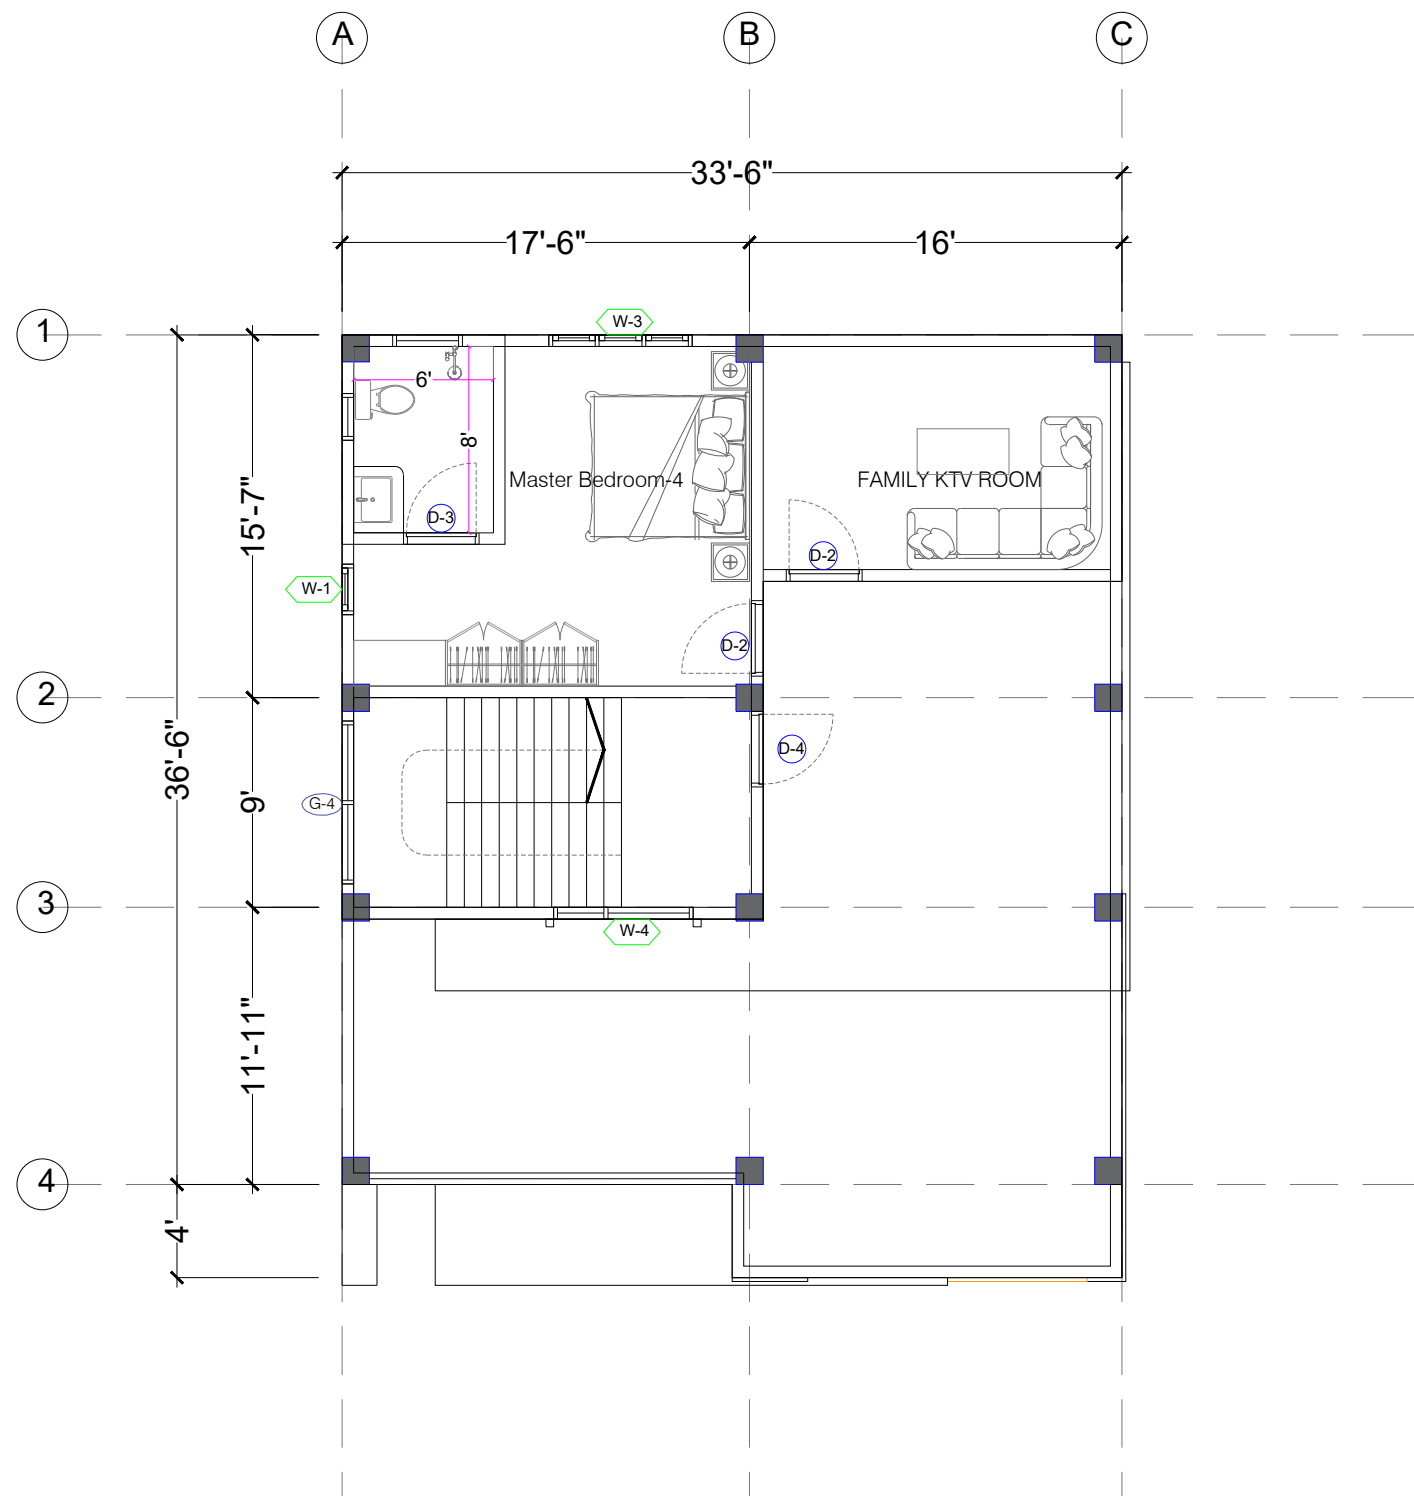

FOOF FLOOR PLAN

OWNER / APPLICANT

PROJECT

PROPOSED
(4) STOREYED
R.C.C BUILDING

BLOCK NO.

LOT NO.

MAGWAY TOWNSHIP

SUBJECT

ROOF FLOOR PLAN

SCALE

AS SHOWN.

SHEET NO.

DATE


7.02.2026

03

L.S

L.C

S.E.C

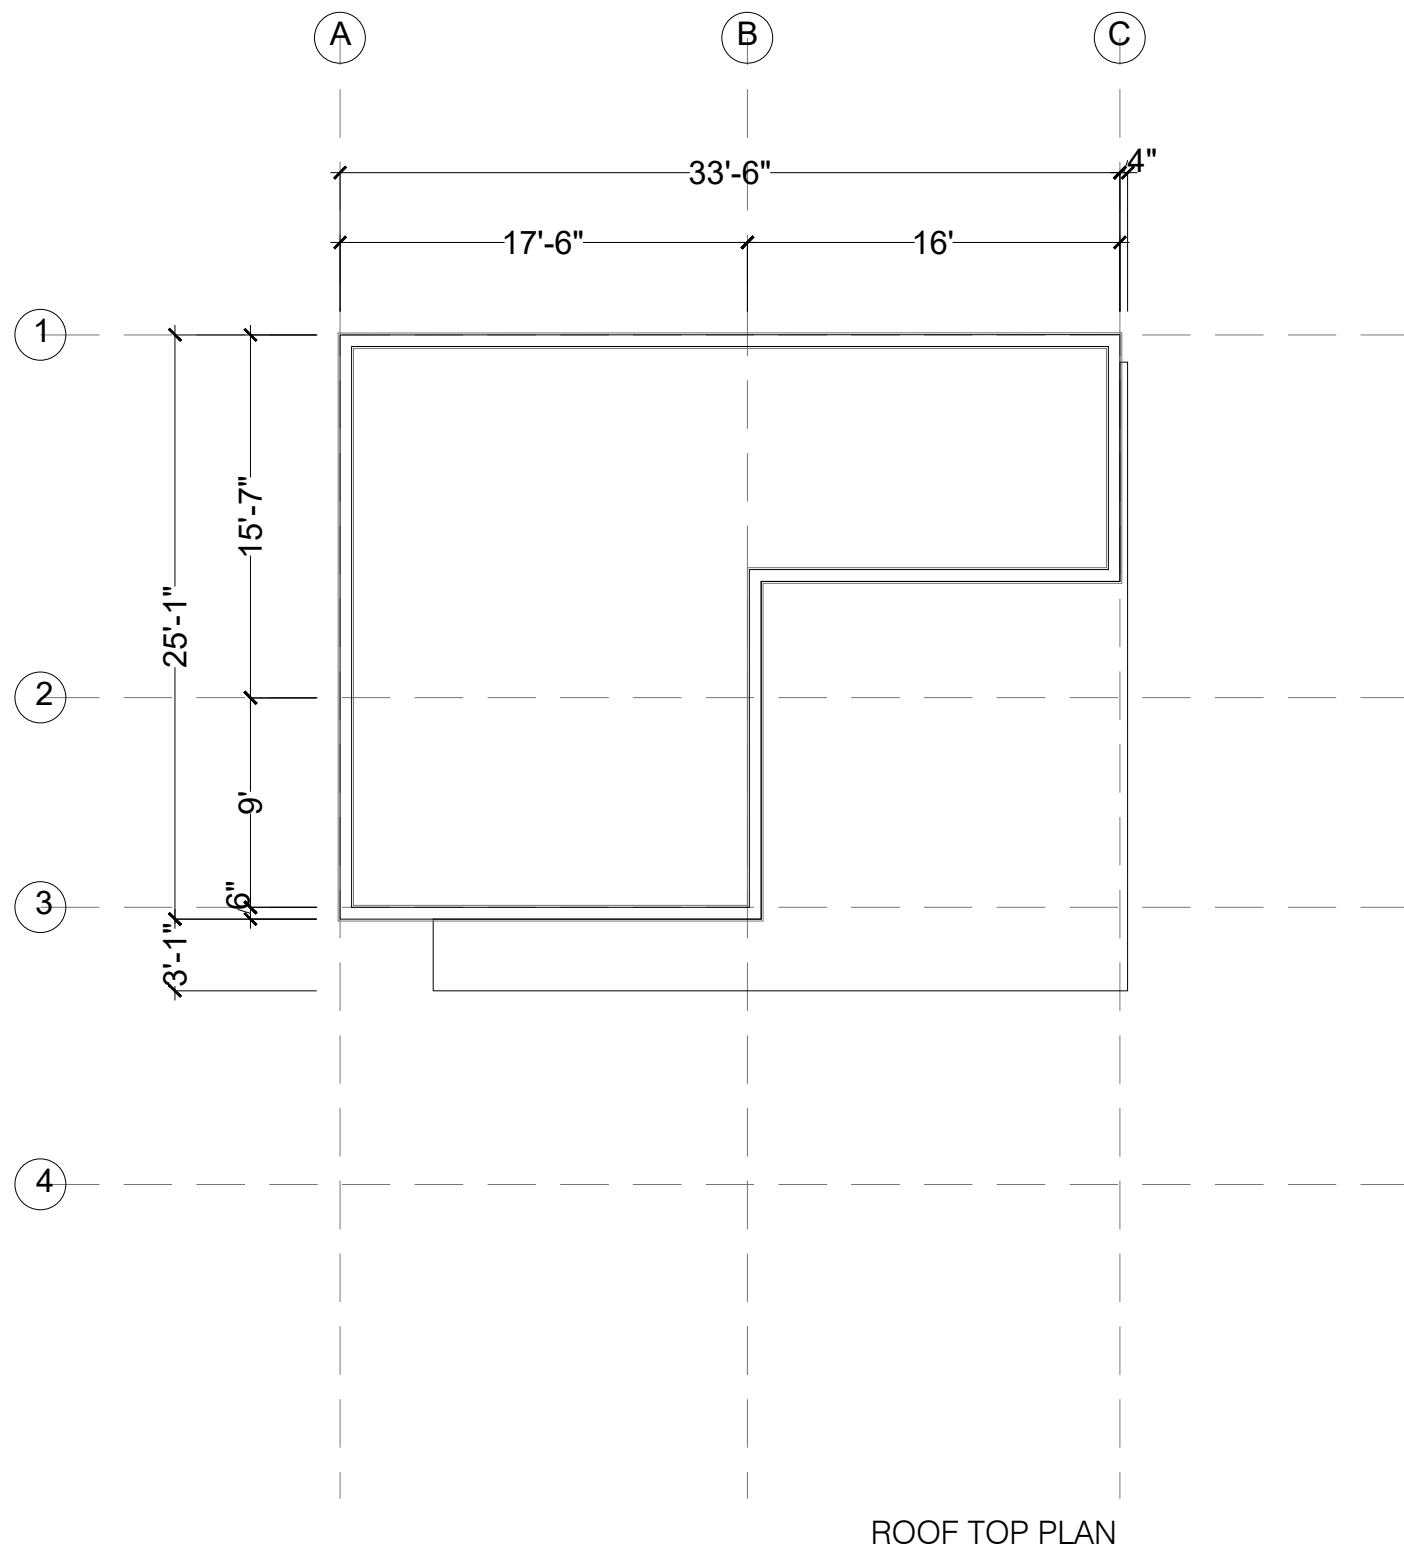

OWNER / APPLICANT

PROJECT
PROPOSED
(4) STOREYED
R.C.C BUILDING

BLOCK NO.

LOT NO.

MAGWAY TOWNSHIP

SUBJECT
ROOF TOP PLAN

SCALE
AS SHOWN.

DATE
7.02.2026

SHEET NO.

04

L.S

L.C

S.E.C



OWNER / APPLICANT

PROJECT	PROPOSED (4) STOREYED R.C.C BUILDING	
	BLOCK NO.	
	LOT NO.	
	MAGWAY TOWNSHIP	


SUBJECT	ELEVATION-1	
---------	-------------	--

SCALE	AS SHOWN.	SHEET NO. 05
DATE	7.02.2026	


L.S

L.C

S.E.C

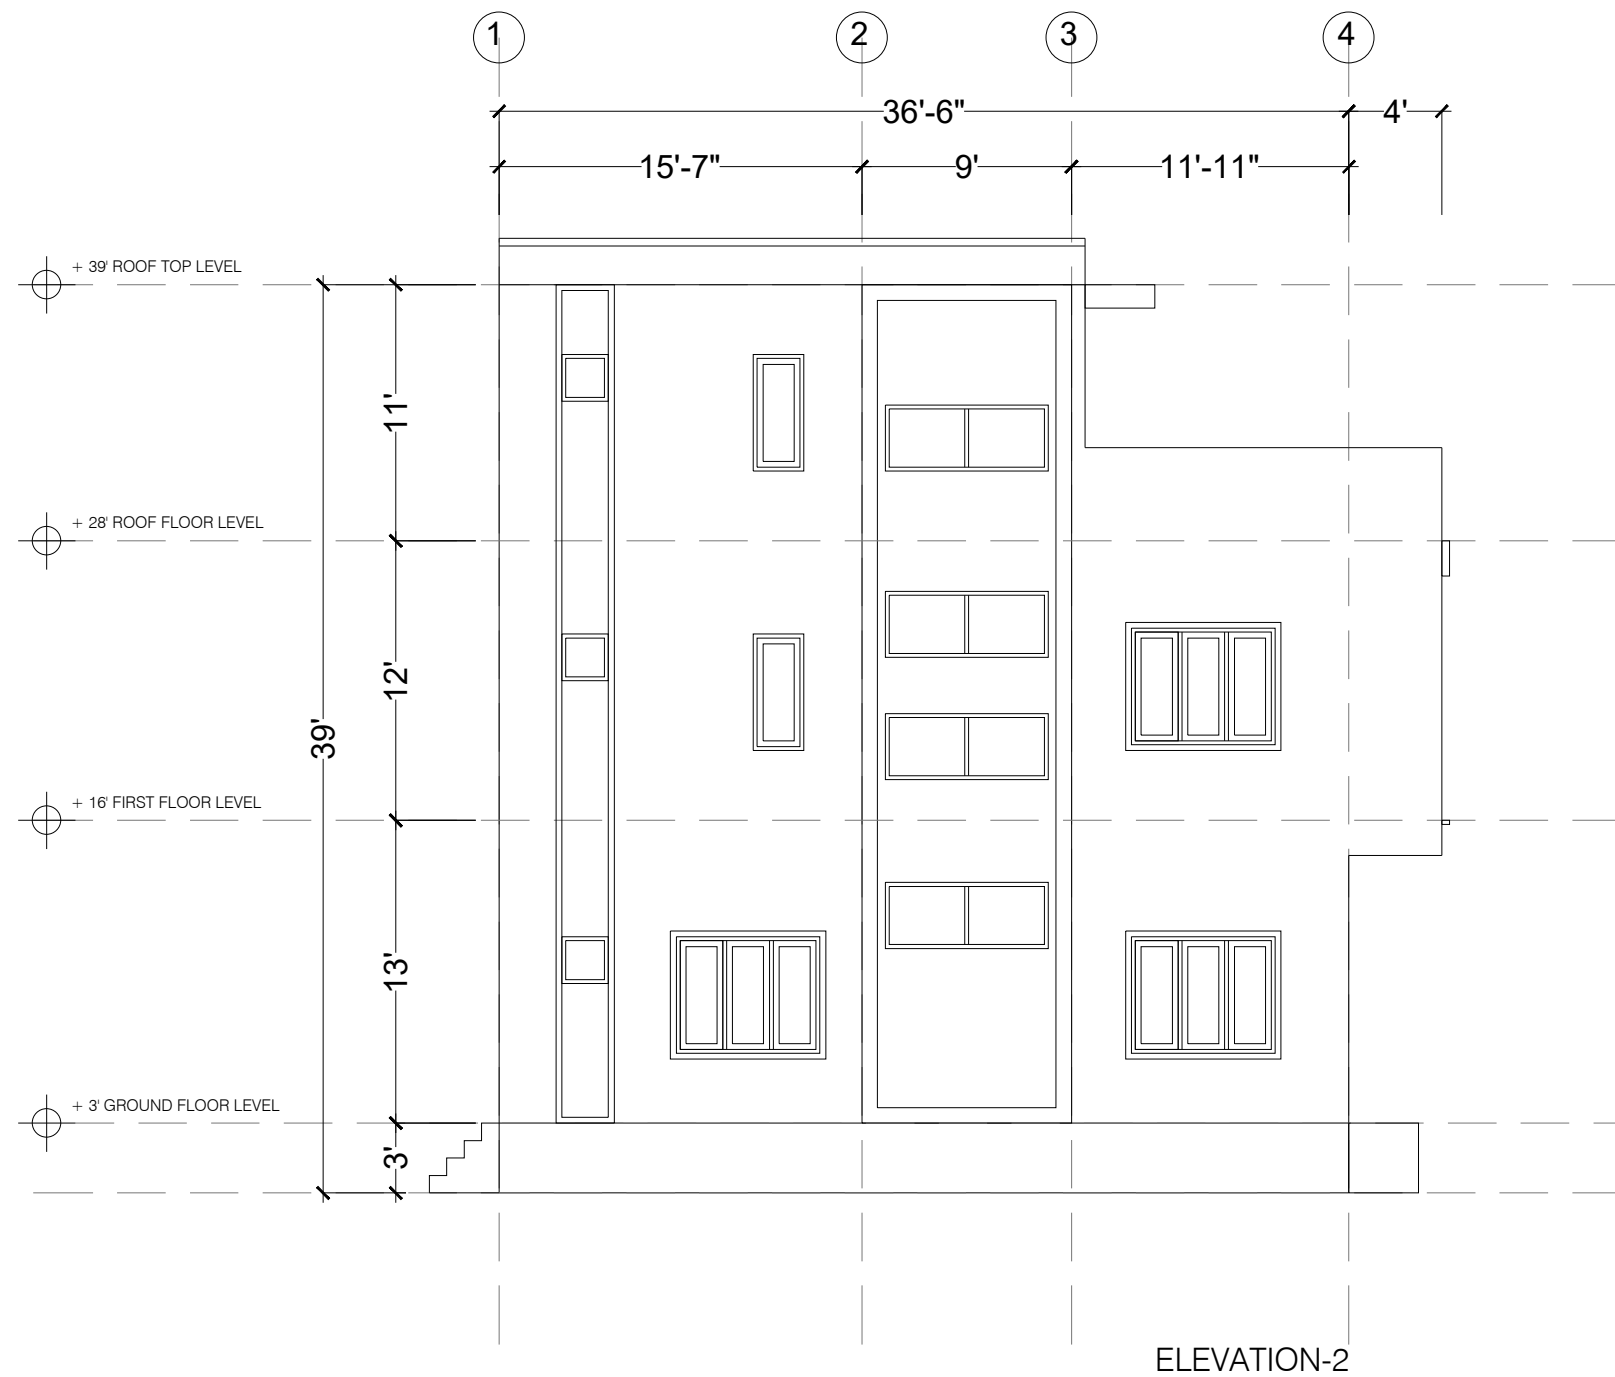

OWNER / APPLICANT		
PROJECT	PROPOSED (4) STOREYED R.C.C BUILDING	
	BLOCK NO.	
	LOT NO.	
	MAGWAY TOWNSHIP	
SUBJECT	ELEVATION-2	
SCALE	AS SHOWN.	SHEET NO. 06
DATE	7.02.2026	
L.S		
L.C		
S.E.C		

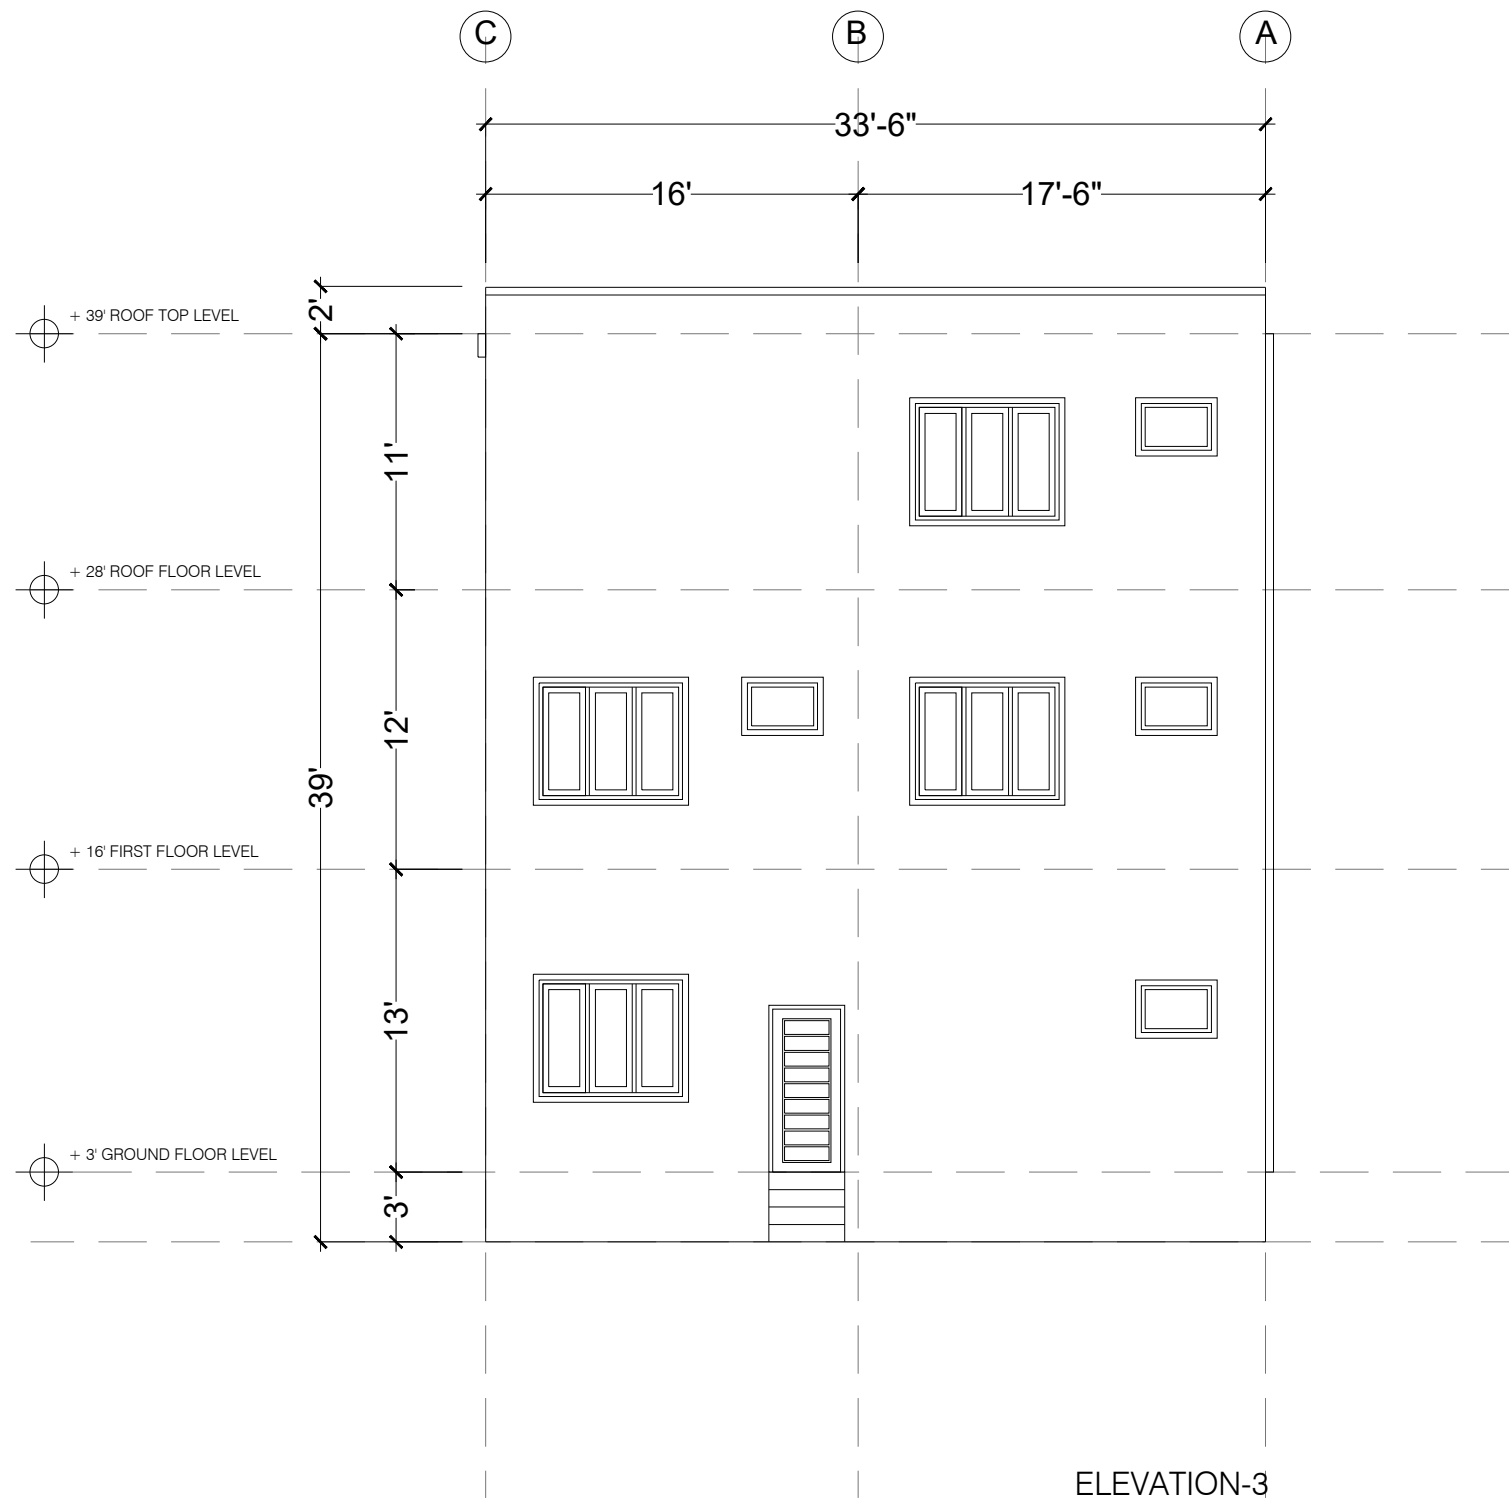

OWNER / APPLICANT

PROJECT
PROPOSED
(4) STOREYED
R.C.C BUILDING

BLOCK NO.

LOT NO.

MAGWAY TOWNSHIP

SUBJECT
ELEVATION-3

SCALE
AS SHOWN.

SHEET NO.


DATE
7.02.2026

07


L.S

L.C


S.E.C

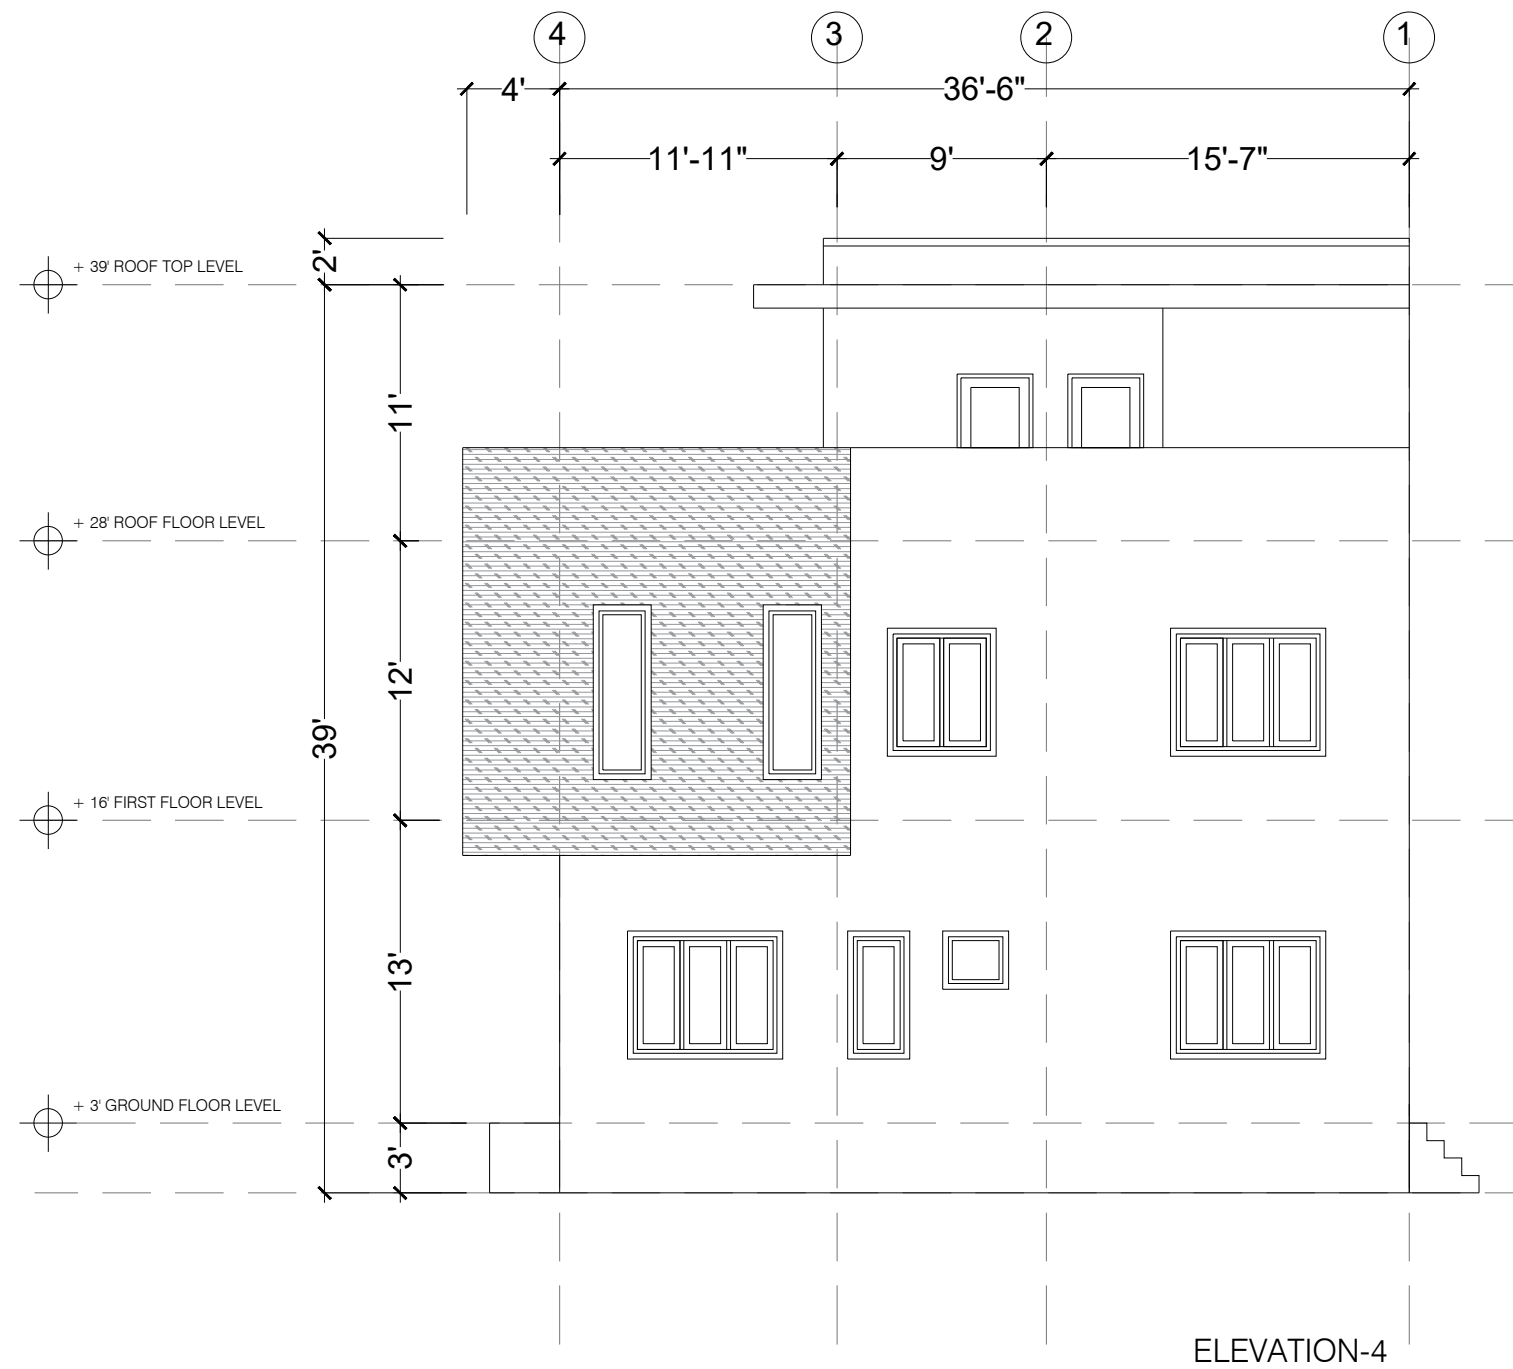


OWNER / APPLICANT		
PROJECT	PROPOSED (4) STOREYED R.C.C BUILDING	
	BLOCK NO.	
	LOT NO.	
	MAGWAY TOWNSHIP	
SUBJECT	ELEVATION-4	
SCALE	AS SHOWN.	SHEET NO. 08
DATE	7.02.2026	
L.S		
L.C		
S.E.C		

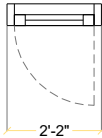


PLAN VIEW

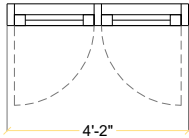


PLAN VIEW

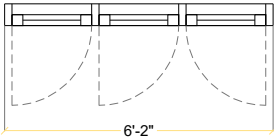

PLAN VIEW

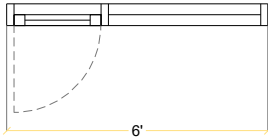

PLAN VIEW

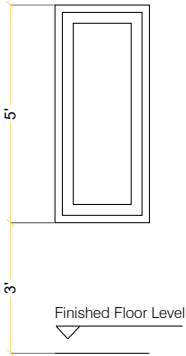


ELEVATION VIEW

WINDOW-1

2' 2" X 5'

ALU: & GLASS

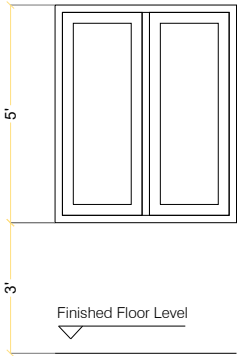


ELEVATION VIEW

WINDOW-2

4' 2" X 5'

ALU: & GLASS

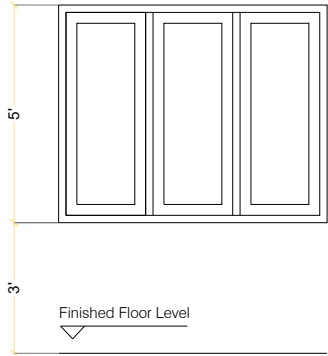


ELEVATION VIEW

WINDOW-3

6' 2" X 5'

ALU: & GLASS

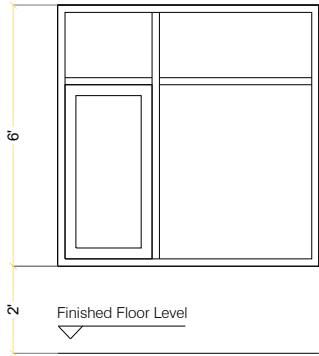

ELEVATION VIEW

WINDOW-4

6' X 6'

ALU: & GLASS

WINDOW 1,2,3,4

OWNER / APPLICANT

PROJECT	PROPOSED (4) STOREYED R.C.C BUILDING	
	BLOCK NO.	
	LOT NO.	
	MAGWAY TOWNSHIP	


SUBJECT	WINDOW 1,2,3,4	
---------	----------------	--

SCALE	AS SHOWN.	SHEET NO. 09
DATE	7.02.2026	


L.S

L.C

S.E.C

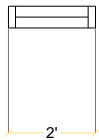

PLAN VIEW

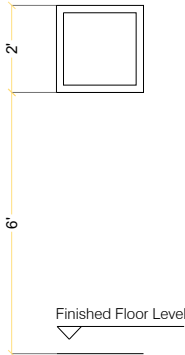


ELEVATION VIEW


GLASS PANEL-1

2' X 2'

ALU: & GLASS

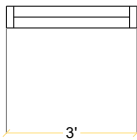

PLAN VIEW

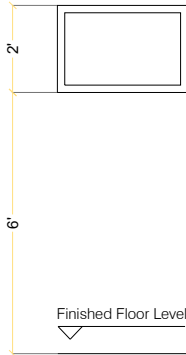


ELEVATION VIEW


GLASS PANEL-2

3' X 2'

ALU: & GLASS

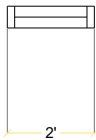

PLAN VIEW

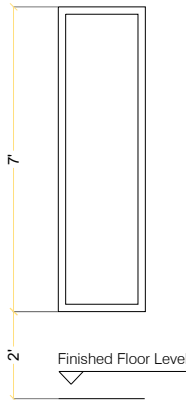


ELEVATION VIEW


GLASS PANEL-3

2' X 7'

ALU: & GLASS

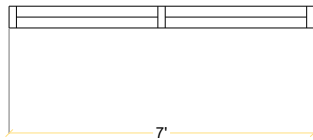

PLAN VIEW

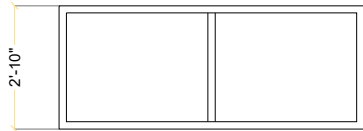

ELEVATION VIEW

GLASS PANEL-4

7' X 2' 10"

ALU: & GLASS

GLASS PANEL 1,2,3,4

OWNER / APPLICANT

PROJECT

PROPOSED
(4) STOREYED
R.C.C BUILDING

BLOCK NO.

LOT NO.

MAGWAY TOWNSHIP

SUBJECT

GLASS PANEL 1,2,3,4

SCALE

AS SHOWN.

SHEET NO.

DATE


7.02.2026

10


L.S

L.C


S.E.C

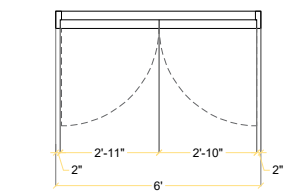


PLAN VIEW

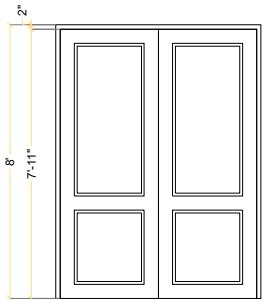


ELEVATION VIEW
DOOR-1
6' X 8'
HARD WOOD
EXTERIOR DOOR

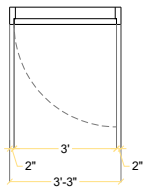


PLAN VIEW

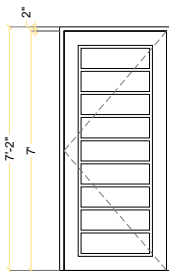


ELEVATION VIEW
DOOR-2
3' 3"X 7' 2"
HARD WOOD
INTERIOR DOOR

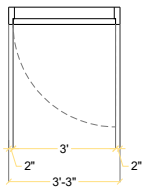


PLAN VIEW

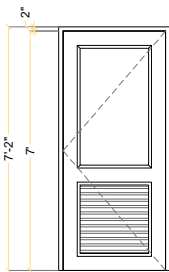


ELEVATION VIEW
DOOR-3
3' 3"X 7' 2"
READY MADE DOOR
INTERIOR DOOR

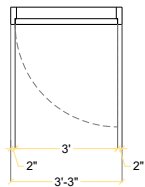


PLAN VIEW

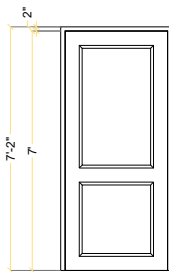

ELEVATION VIEW
DOOR-4
3' 3"X 7' 2"
READY MADE DOOR
EXTERIOR DOOR

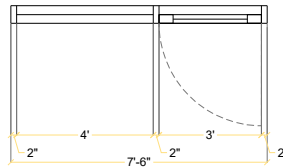

PLAN VIEW

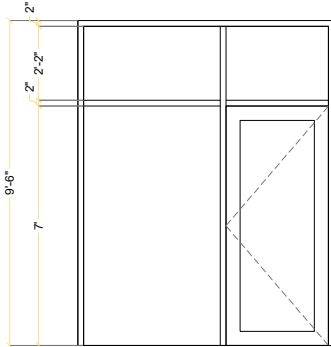

ELEVATION VIEW
DOOR-5
7' 6"X 9' 6"
ALU:& GLASS
EXTERIOR DOOR

DOOR 1,2,3,4,5

OWNER / APPLICANT

PROJECT
**PROPOSED
(4) STOREYED
R.C.C BUILDING**

BLOCK NO.

LOT NO.

MAGWAY TOWNSHIP

SUBJECT
DOOR 1,2,3,4,5

SCALE
AS SHOWN.

DATE
7.02.2026


SHEET NO.

11


L.S

L.C


S.E.C

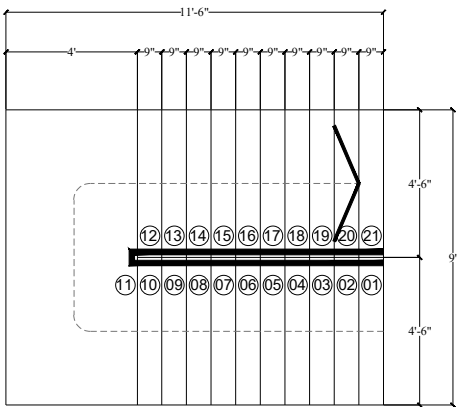

PLAN VIEW

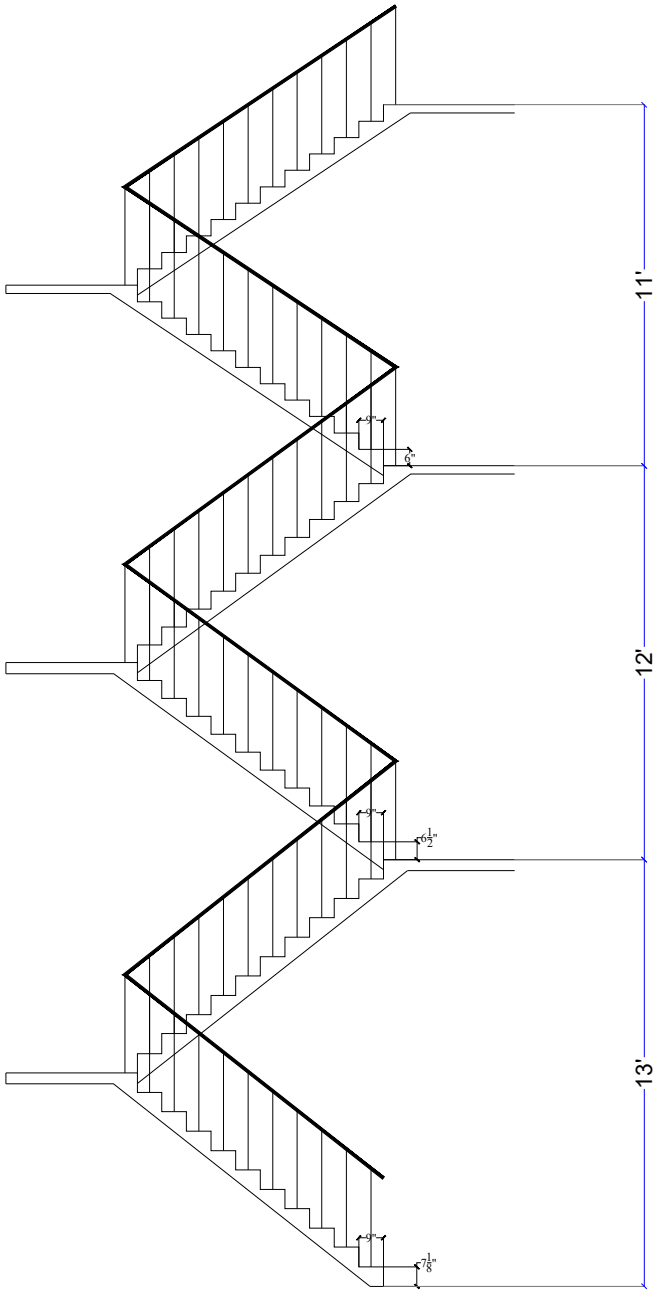

ELEVATION VIEW

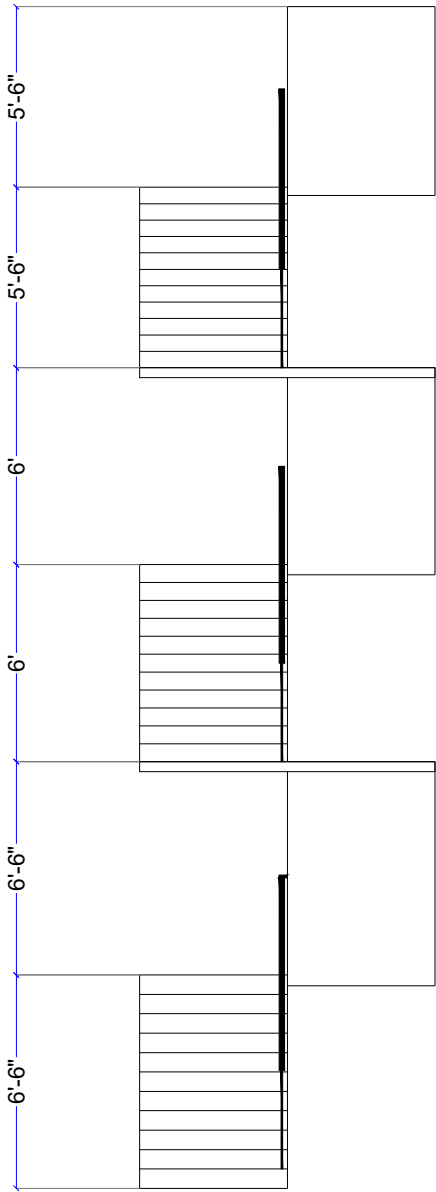

FRONT VIEW

STAIR DETAILS

OWNER / APPLICANT

PROJECT	PROPOSED (4) STOREYED R.C.C BUILDING	
	BLOCK NO.	
	LOT NO.	
	MAGWAY TOWNSHIP	

SUBJECT	STAIR DETAILS	
---------	---------------	--

SCALE	AS SHOWN.	SHEET NO. 12
DATE	7.02.2026	

L.S

L.C

S.E.C